
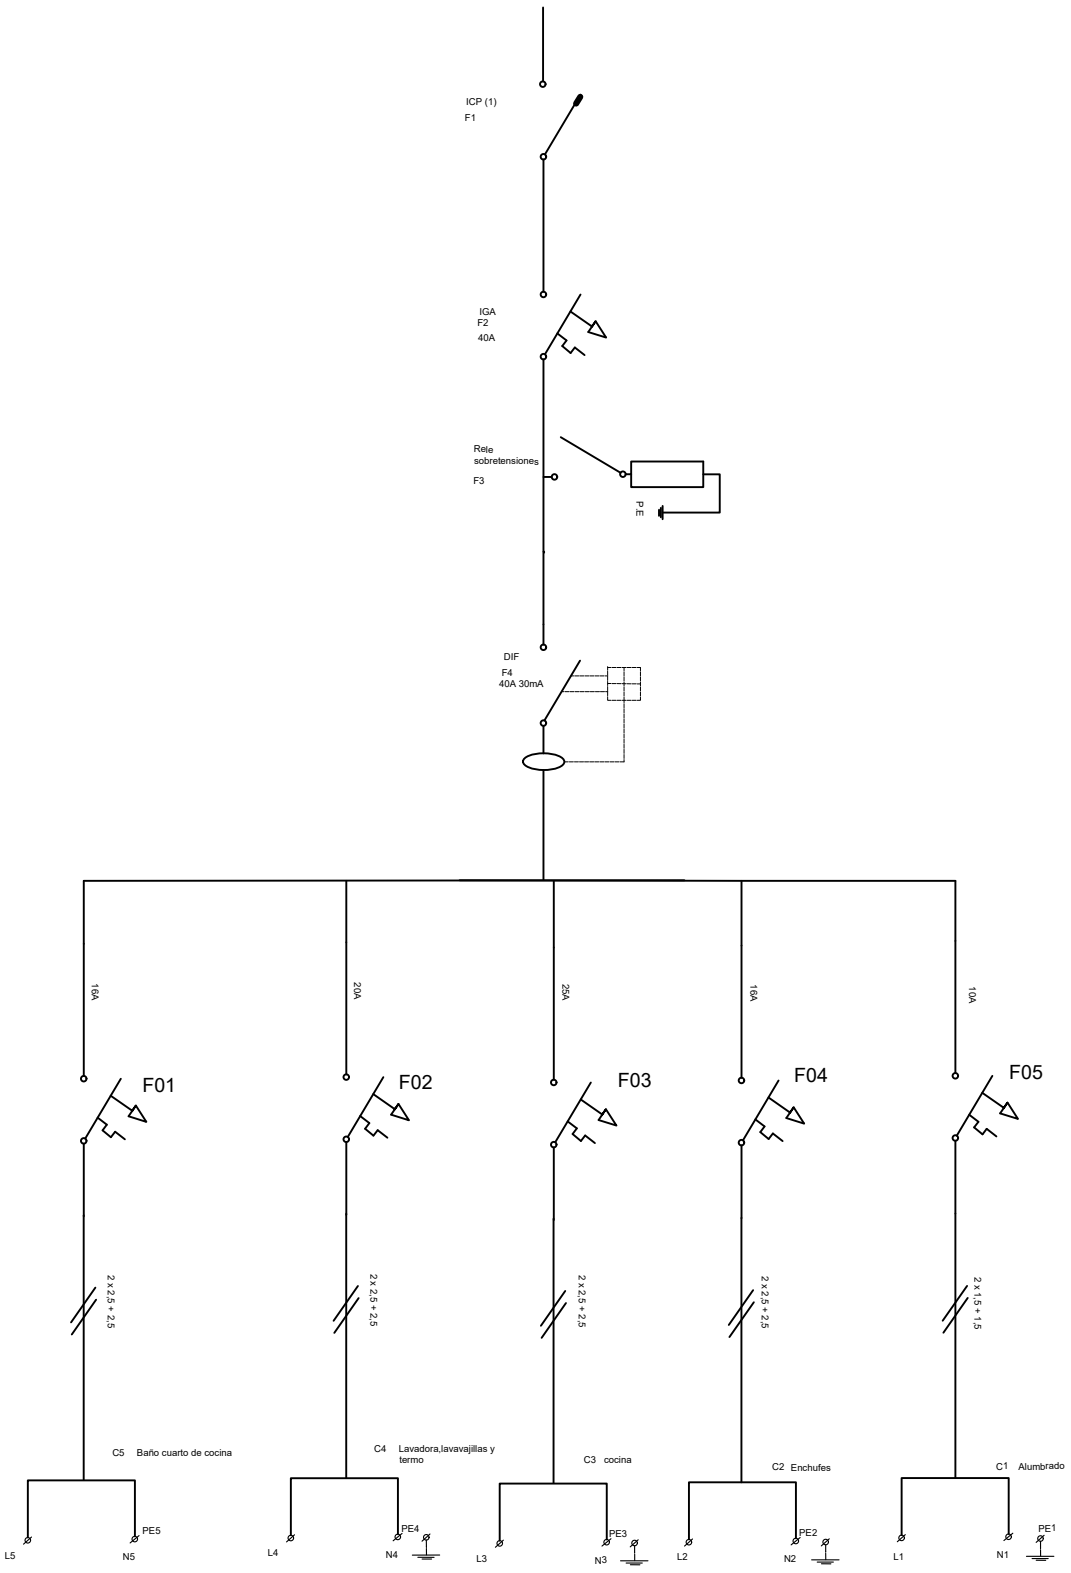


	Fecha	Nombre	Firmas
Dibujado			
Combrobado			
Escala			


JESUÏTES El Clot
Escola del Clot

Numero
Sustituye a
Sustituido por


C1

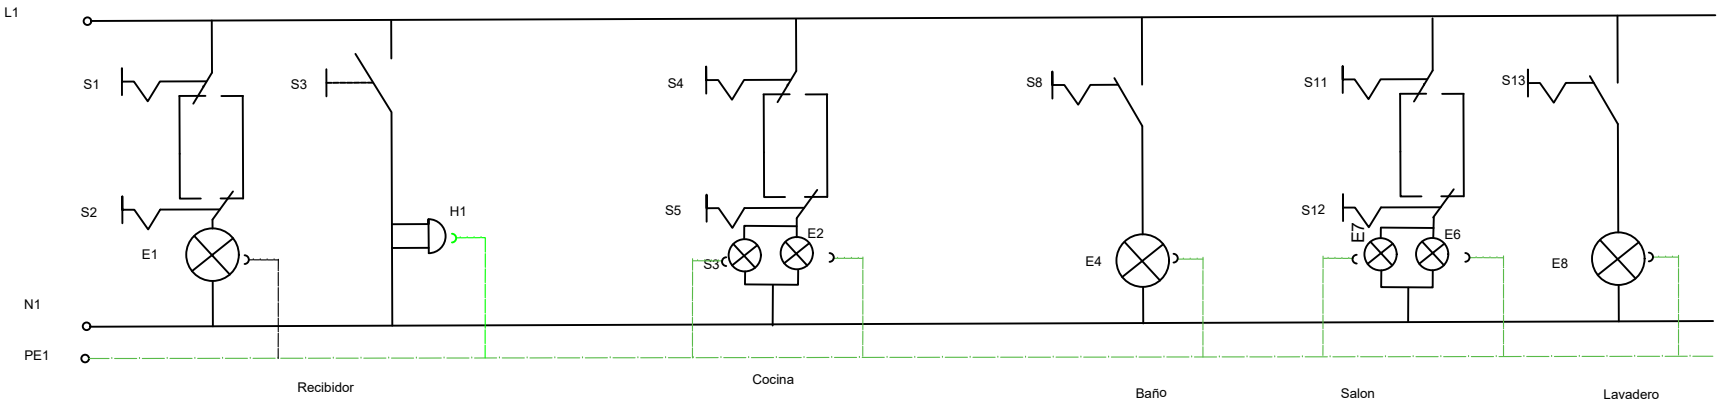

C2

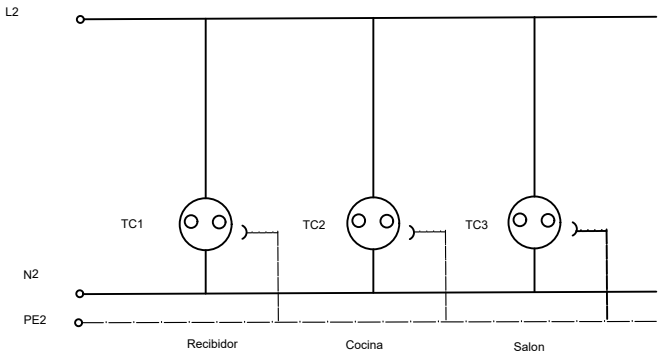


C3

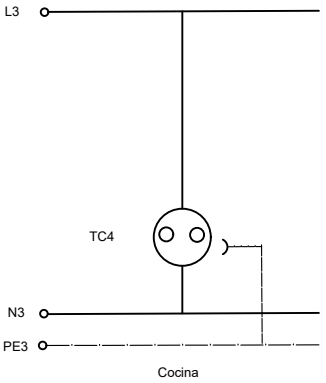


JESUÏTES El Clot Escola del Clot	ALUMNE / GRUP	PROJECTE	TITOL PLANOL	REV	CONCEPTE	DATA NOM	REF / DATA PLANOL Nº / ESCALA

C4

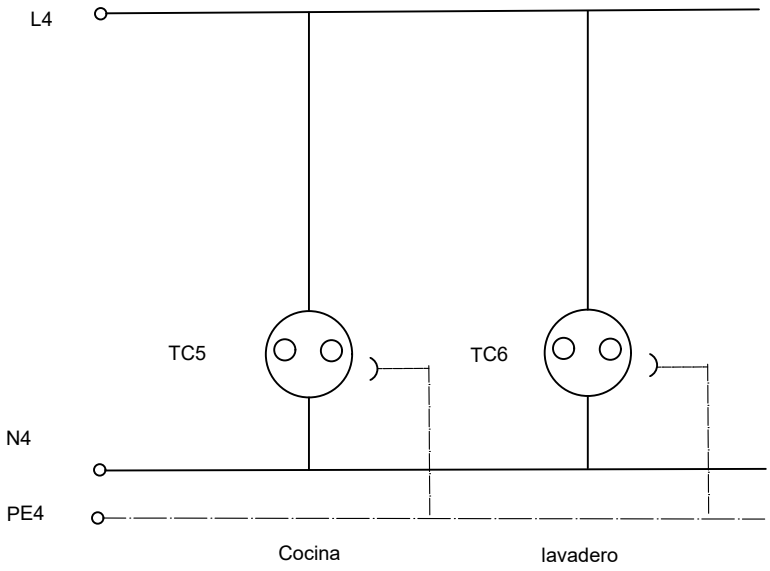

C5

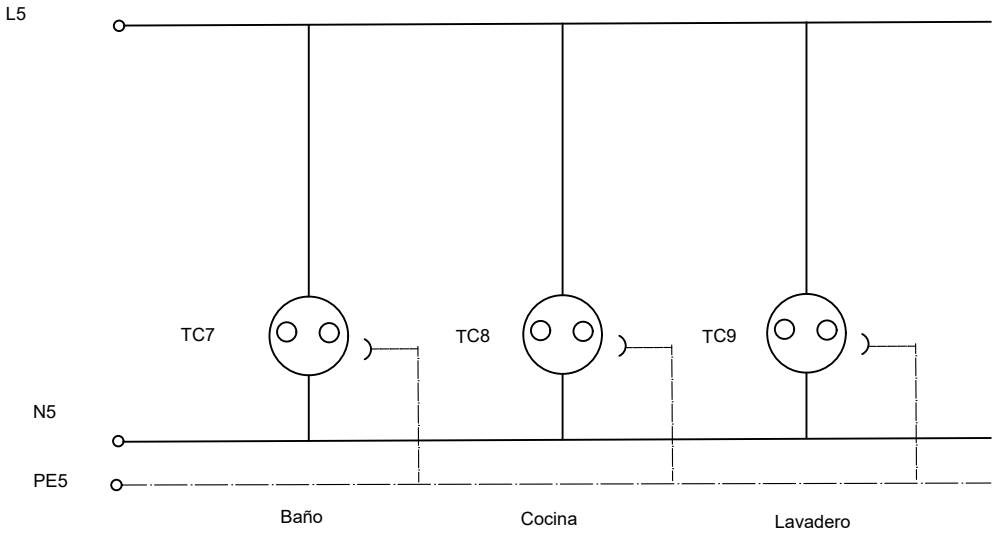

	Fecha	Nombre	Firmas	JESUÏTES El Clot Escola del Clot	
Dibujado					
Comprobado					
Escala	(Nombre del plano)				Numero
					Sustituye a
					Sustituido por.